

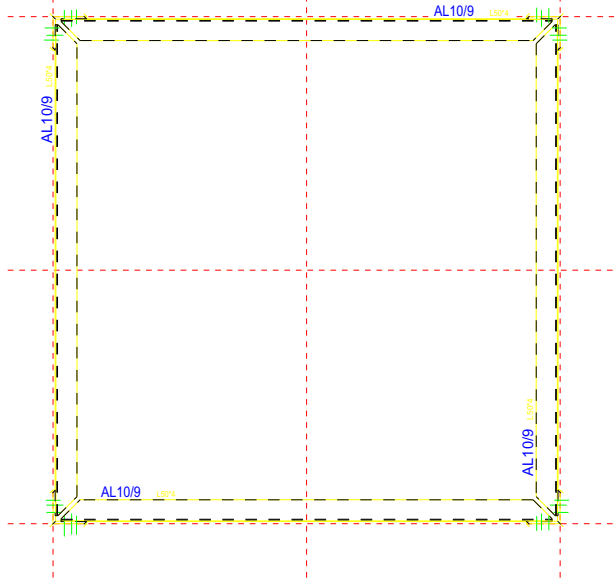


POZ	NO	PROFIL	KALITE
AL101	1	L50/4	S235JR
AL102	1	L50/4	S235JR
AL103	1	L50/4	S235JR
AL104	1	L50/4	S235JR
AL105	1	L50/4	S235JR
AL106	1	L50/4	S235JR
AL107	1	L50/4	S235JR
AL108	1	L50/4	S235JR
AL109	4	L50/4	S235JR
AL1010	2	L40/4	S235JR
AL1011	2	L40/4	S235JR
AL1012	2	L40/4	S235JR
AL1013	8	L40/4	S235JR
AL1014	8	L40/4	S235JR
AL1015	4	L40/4	S235JR
AL1016	8	PL8/70	S355JR
AL1017	4	L40/4	S235JR
AL1018	4	L40/4	S235JR
AL1019	4	L40/4	S235JR
AL1020	4	L40/4	S235JR
AL1021	4	L40/4	S235JR
AL1022	4	L40/4	S235JR
AL1023	4	L40/4	S235JR
AL1024	4	L40/4	S235JR
AL1025	4	L40/4	S235JR
AL1026	4	L40/4	S235JR
AL1027	4	L40/4	S235JR
AL1028	4	L40/4	S235JR
AL1029	1	L40/4	S235JR
AL1030	1	L40/4	S235JR
AL1031	1	D15	S235JR
AL1032	2	PL4*303	S235JR
AL1033	1	PL4*740	S235JR
AL1034	1	PL4*248	S235JR
AL1035	4	L80/5	S355JR
AL1036	4	L80/5	S355JR
AL1037	4	PL8/70	S355JR
AL1038	4	L80/5	S355JR
AL1039	1	PL10/65	S235JR
AL1040	1	L80/5	S235JR
AL1041	1	L80/5	S235JR
AL1042	1	L80/5	S235JR
AL1043	1	L80/5	S235JR
AL1044	4	L70/5	S355JR
AL1045	4	PL8/70	S355JR

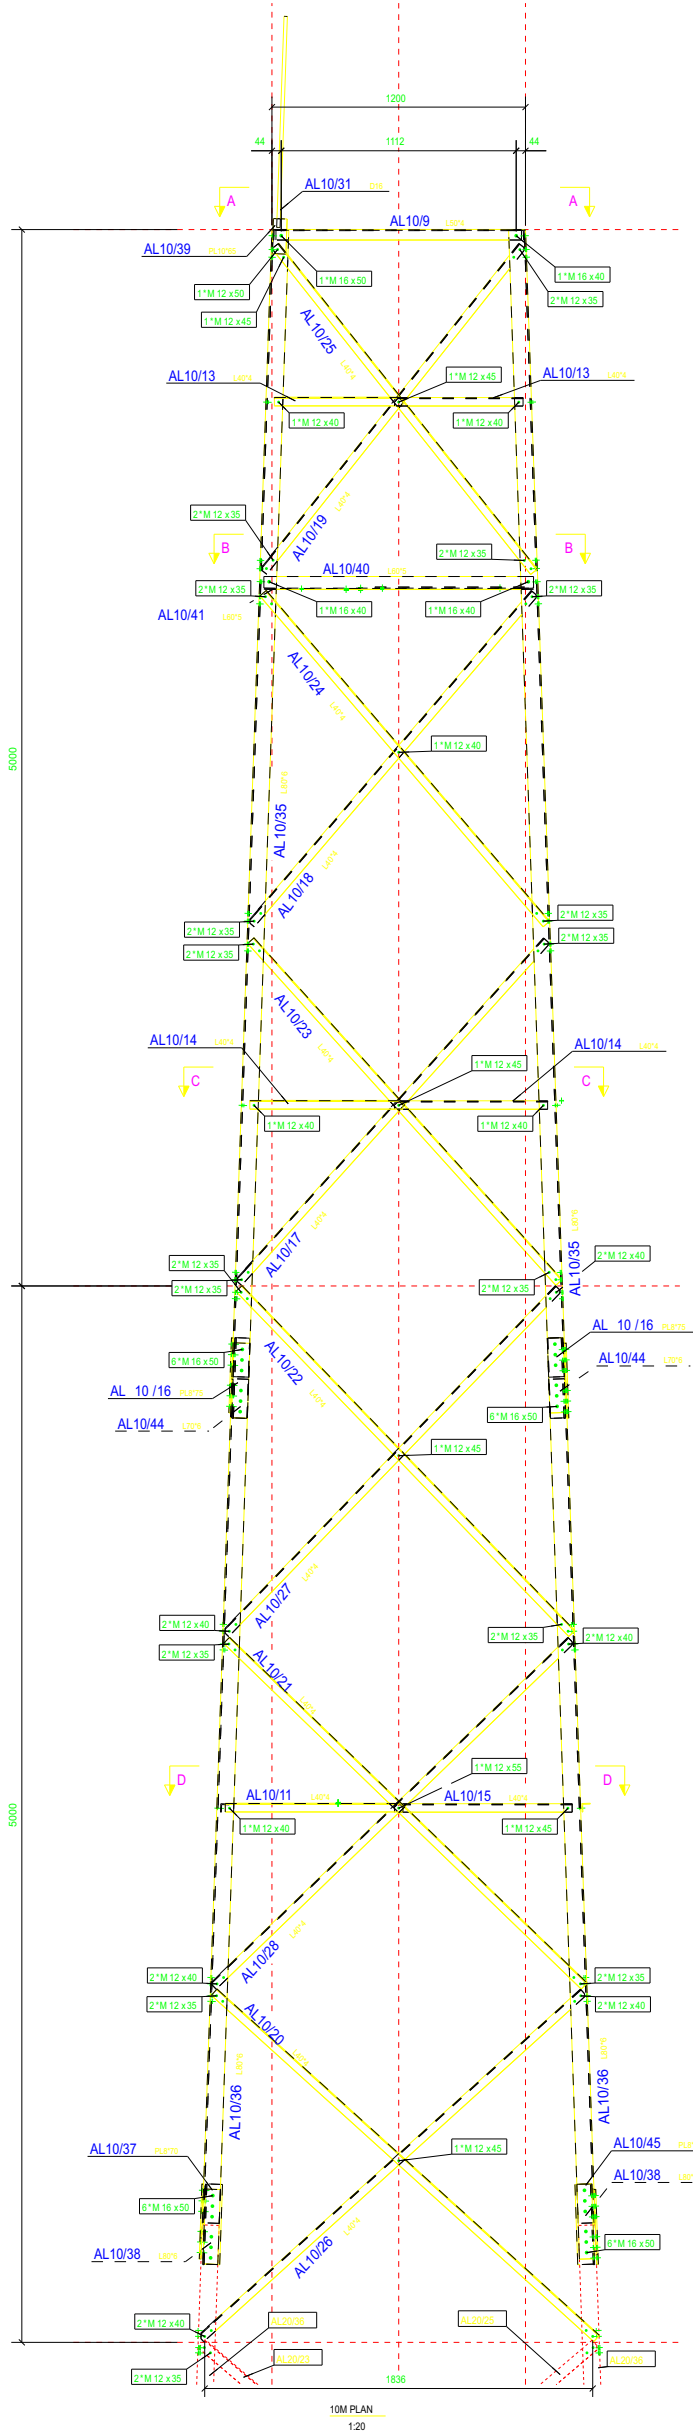


A - A

1:10

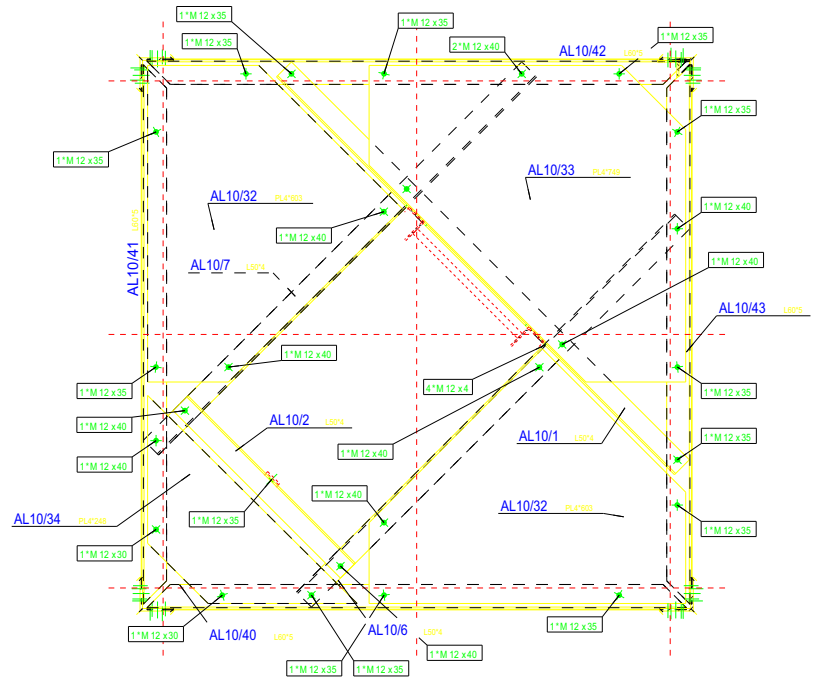


B - B

1:10

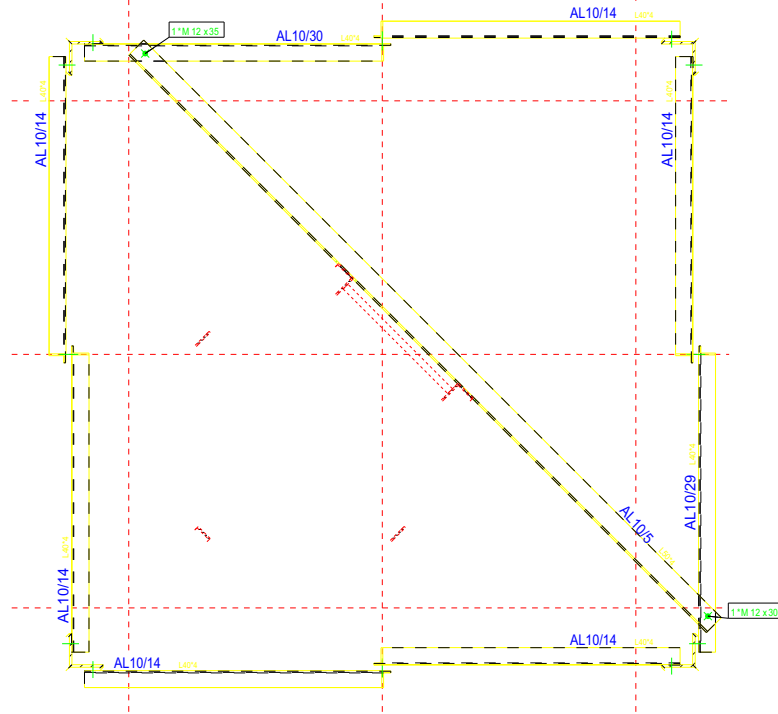

C - C

1:10




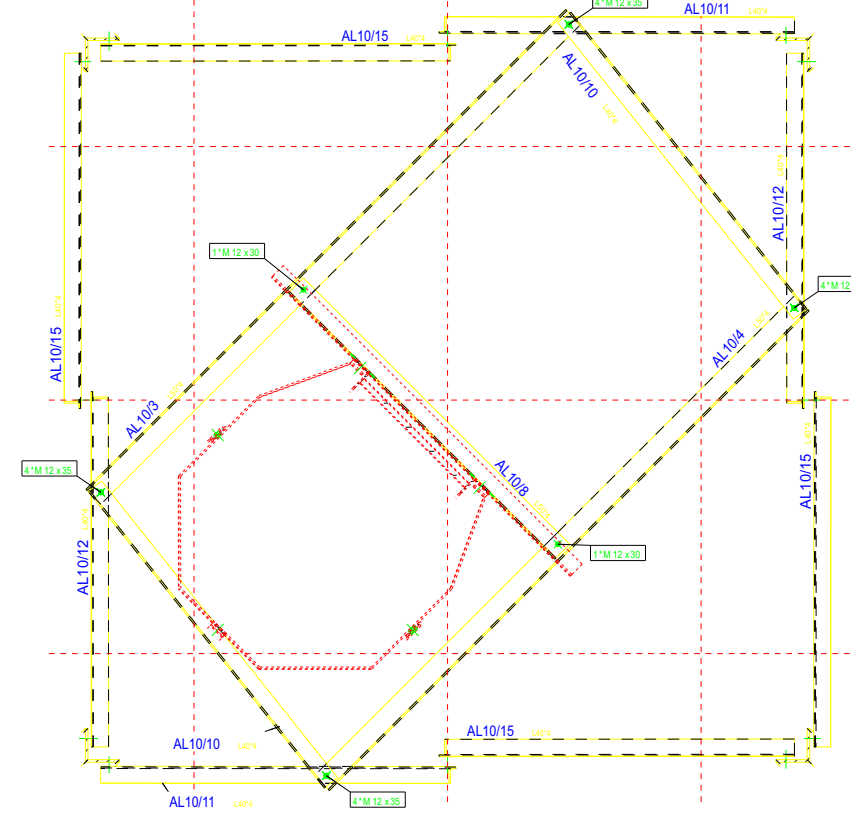


D - D

1:10







1	0	FOR INFORMATION		09.04.2014
NO	REV	AÇIKLAMA		TARİH
TERLEMEZ Machinery		Address: Dağyaka Dist. 2008 St. No: 5 Kazan / Ankara / Turkey		
RESİM NO	30M-160-10-001			
YÜKLENİCİ	30M 160-10			
CİZEN	R BAGLAR	TARİH 29.04.2014		
YUKLENICI NO	30M 160-10	OLCEK	1:10	1:20
DRAWING No	[1]	REVIZYON No.	1	

POZ	NO	PROFIL	KALITE
AL20/1	1	L50/4	S235JR
AL20/2	1	L50/4	S235JR
AL20/3	1	L50/4	S235JR
AL20/4	1	L50/4	S235JR
AL20/5	3	L50/4	S235JR
AL20/6	3	L50/4	S235JR
AL20/7	4	L50/4	S235JR
AL20/8	3	L50/4	S235JR
AL20/9	3	L50/4	S235JR
AL20/10	3	L50/4	S235JR
AL20/11	1	L50/4	S235JR
AL20/12	1	L50/4	S235JR
AL20/13	1	L50/4	S235JR
AL20/14	1	L50/4	S235JR
AL20/15	1	L50/4	S235JR
AL20/16	1	L50/4	S235JR
AL20/17	1	L50/4	S235JR
AL20/18	4	L50/4	S235JR
AL20/19	4	L50/4	S235JR
AL20/20	4	L50/4	S235JR
AL20/21	4	L50/4	S235JR
AL20/22	4	L50/4	S235JR
AL20/23	4	L50/4	S235JR
AL20/24	4	L50/4	S235JR
AL20/25	4	L50/4	S235JR
AL20/26	4	L50/4	S235JR
AL20/27	4	L50/4	S235JR
AL20/28	4	L50/4	S235JR
AL20/29	4	L50/4	S235JR
AL20/30	2	L40/4	S235JR
AL20/31	4	L80/8	S355JR
AL20/32	4	L80/8	S355JR
AL20/33	4	PL10/35	S355JR
AL20/34	4	PL10/35	S355JR
AL20/35	4	PL10/35	S355JR
AL20/36	4	L80/8	S355JR
AL20/37	4	L80/8	S355JR

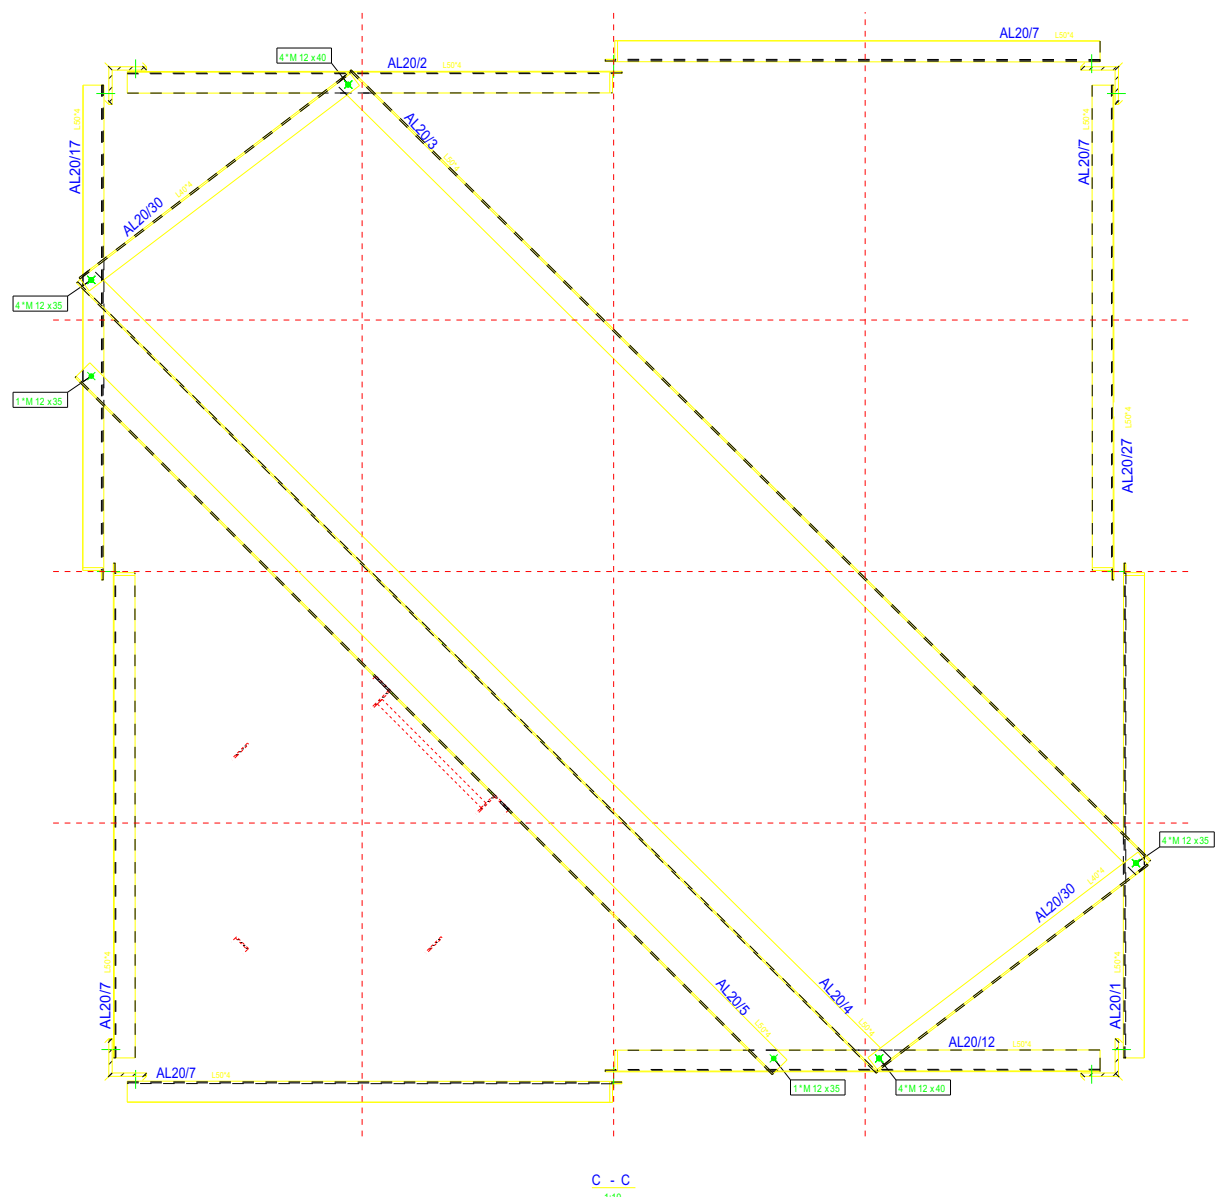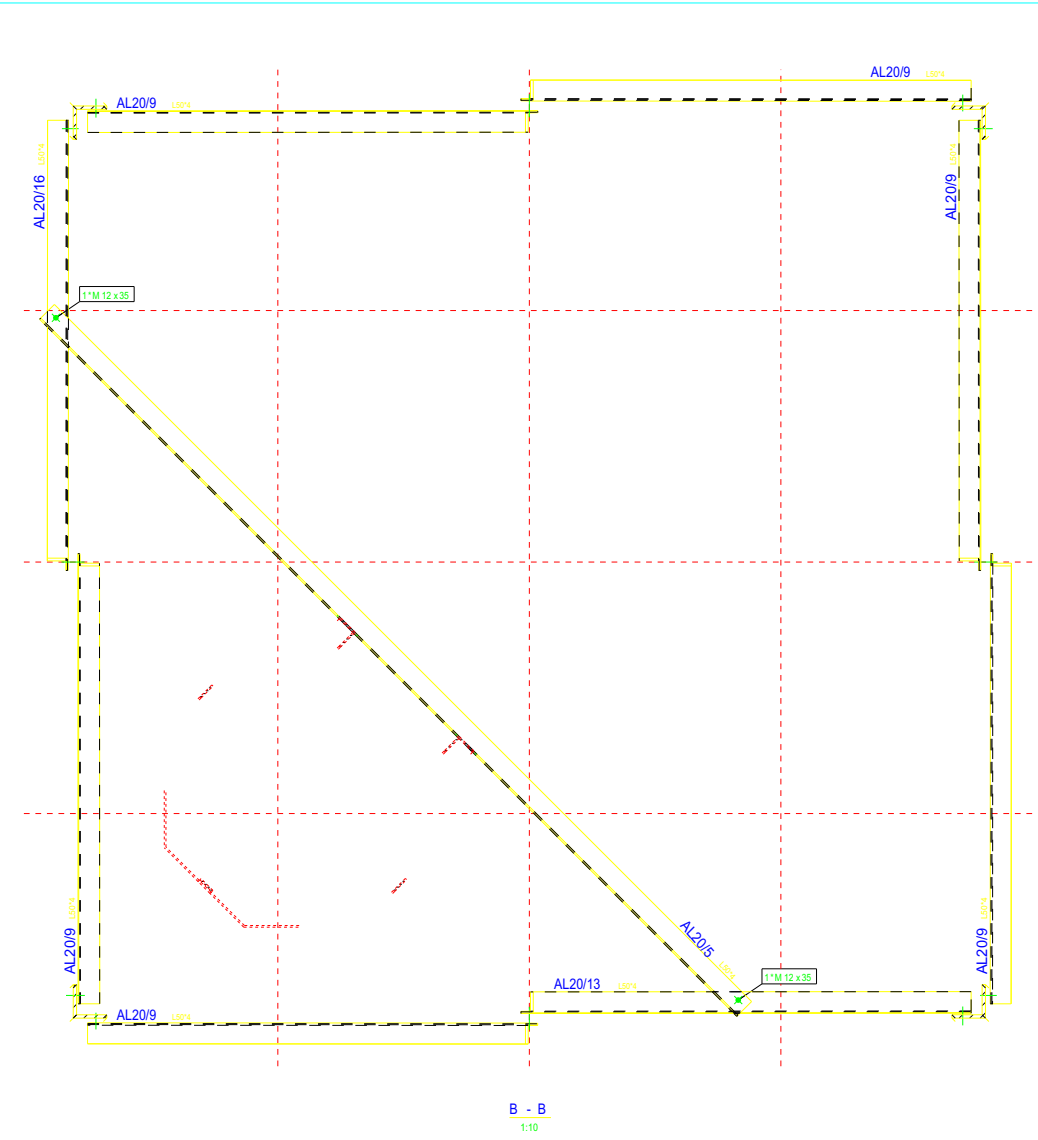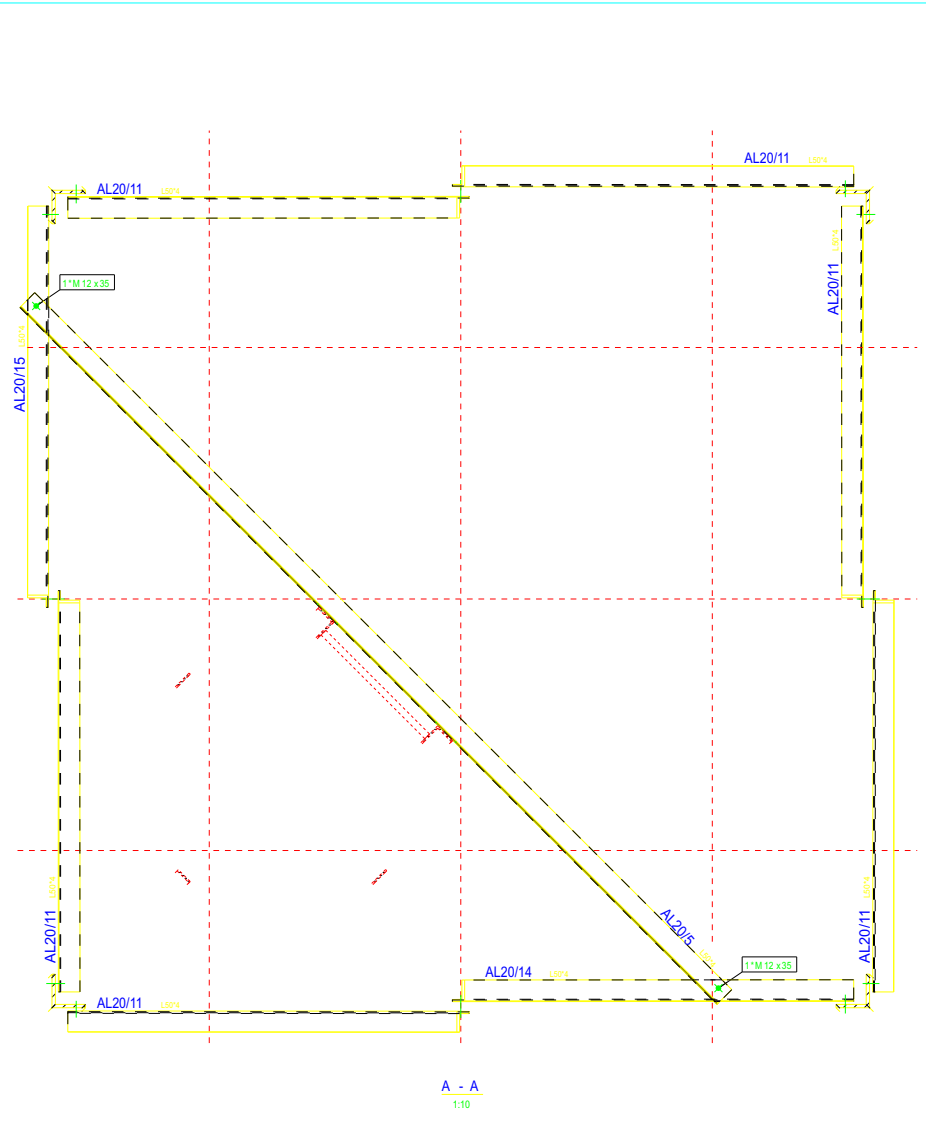
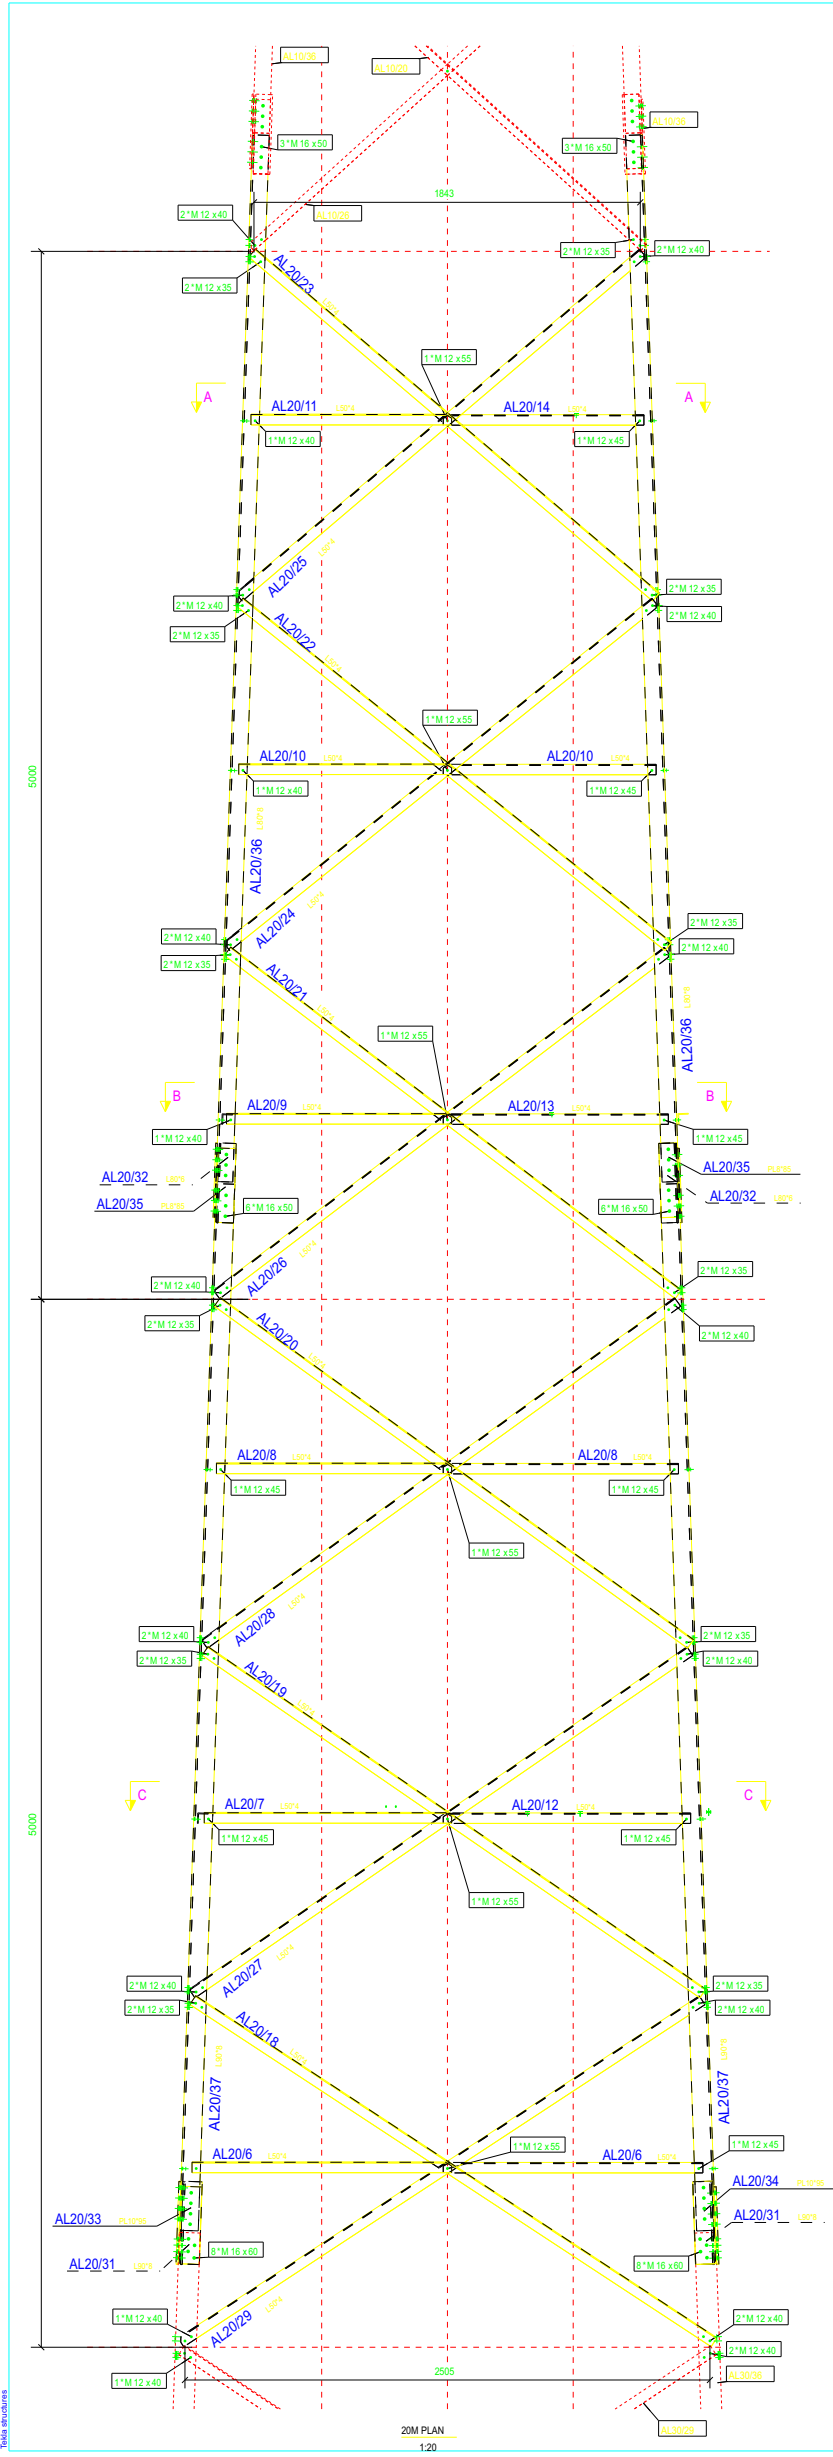


1	0	FOR INFORMATION		09.04.2014
NO	REV	AÇIKLAMA		TARİH
TERLEMEZ Machinery		Address: Dağıyaka Dist. 2008 St. No: 5 Kazan / Ankara / Turkey		
RESİM NO		30M-160-10-002		
YÜKLENİCİ		30M 160-10		
CİZEN		R BAĞLAR	TARİH 29.04.2014	
YÜKLENİCİ NO		30M 160-10	OLÇEK 1:10	1:20
DRAWING No		[2]	REVİZYON No.	1

POZ	NO	PROFIL	KALITE
AL302	8	L50/4	S235JR
AL303	8	L50/4	S235JR
AL304	8	L50/4	S235JR
AL3012	8	L50/4	S235JR
AL3015	8	L50/4	S235JR
AL3018	8	L50/4	S235JR
AL3017	4	L50/4	S235JR
AL3018	4	L50/4	S235JR
AL3019	4	L50/4	S235JR
AL3020	2	L50/4	S235JR
AL3021	2	L50/4	S235JR
AL3022	12	L50/4	S235JR
AL3023	16	L50/4	S235JR
AL3024	12	L50/4	S235JR
AL3025	2	L50/4	S235JR
AL3026	2	L50/4	S235JR
AL3027	2	L50/4	S235JR
AL3028	2	L50/4	S235JR
AL3029	8	L50/4	S235JR
AL3032	8	PL10/115	S355JR
AL3033	8	PL10/115	S355JR
AL3036	8	L100/10	S355JR
AL3038	8	L10/10	S355JR
AL3040	2	L50/4	S235JR
AL3041	3	L50/4	S235JR
AL3042	3	L50/4	S235JR
AL3043	3	L50/4	S235JR
AL3044	1	L50/4	S235JR
AL3045	1	L50/4	S235JR
AL3046	1	L50/4	S235JR
AL3047	1	L50/4	S235JR
AL3048	4	L60/2	S235JR
AL3049	4	L60/2	S235JR
AL3050	4	L60/2	S235JR
AL3051	4	L60/2	S235JR
AL3052	16	L100/10	S355JR
AL3053	16	L100/10	S355JR
AL3054	4	L10/10	S355JR

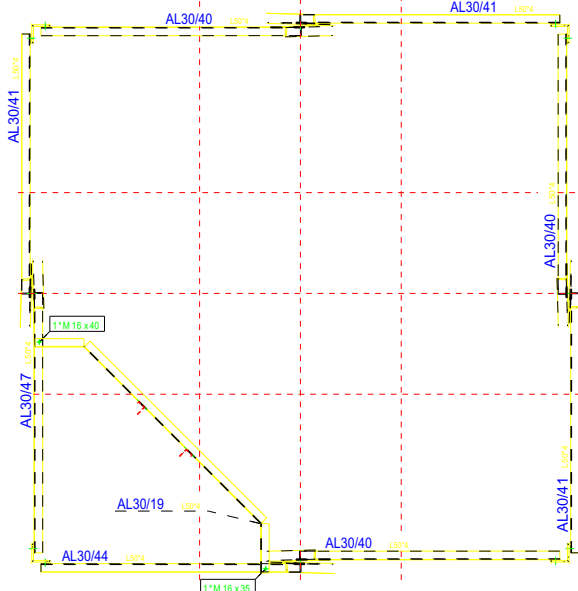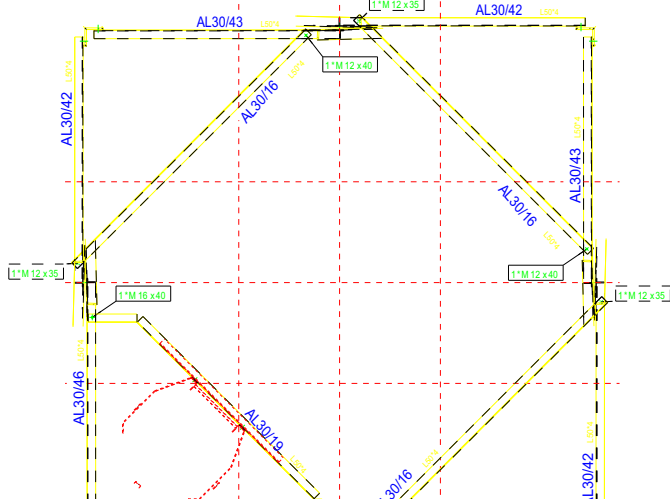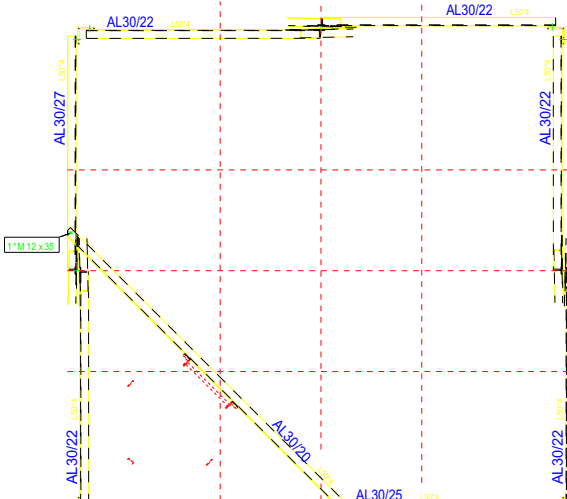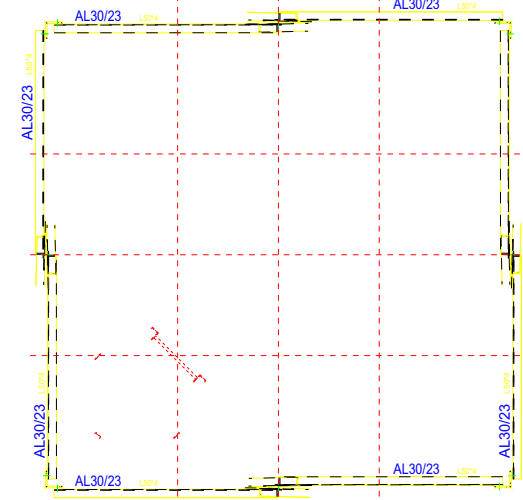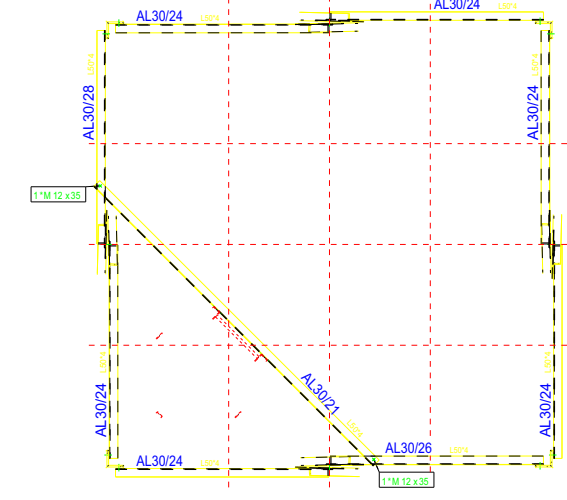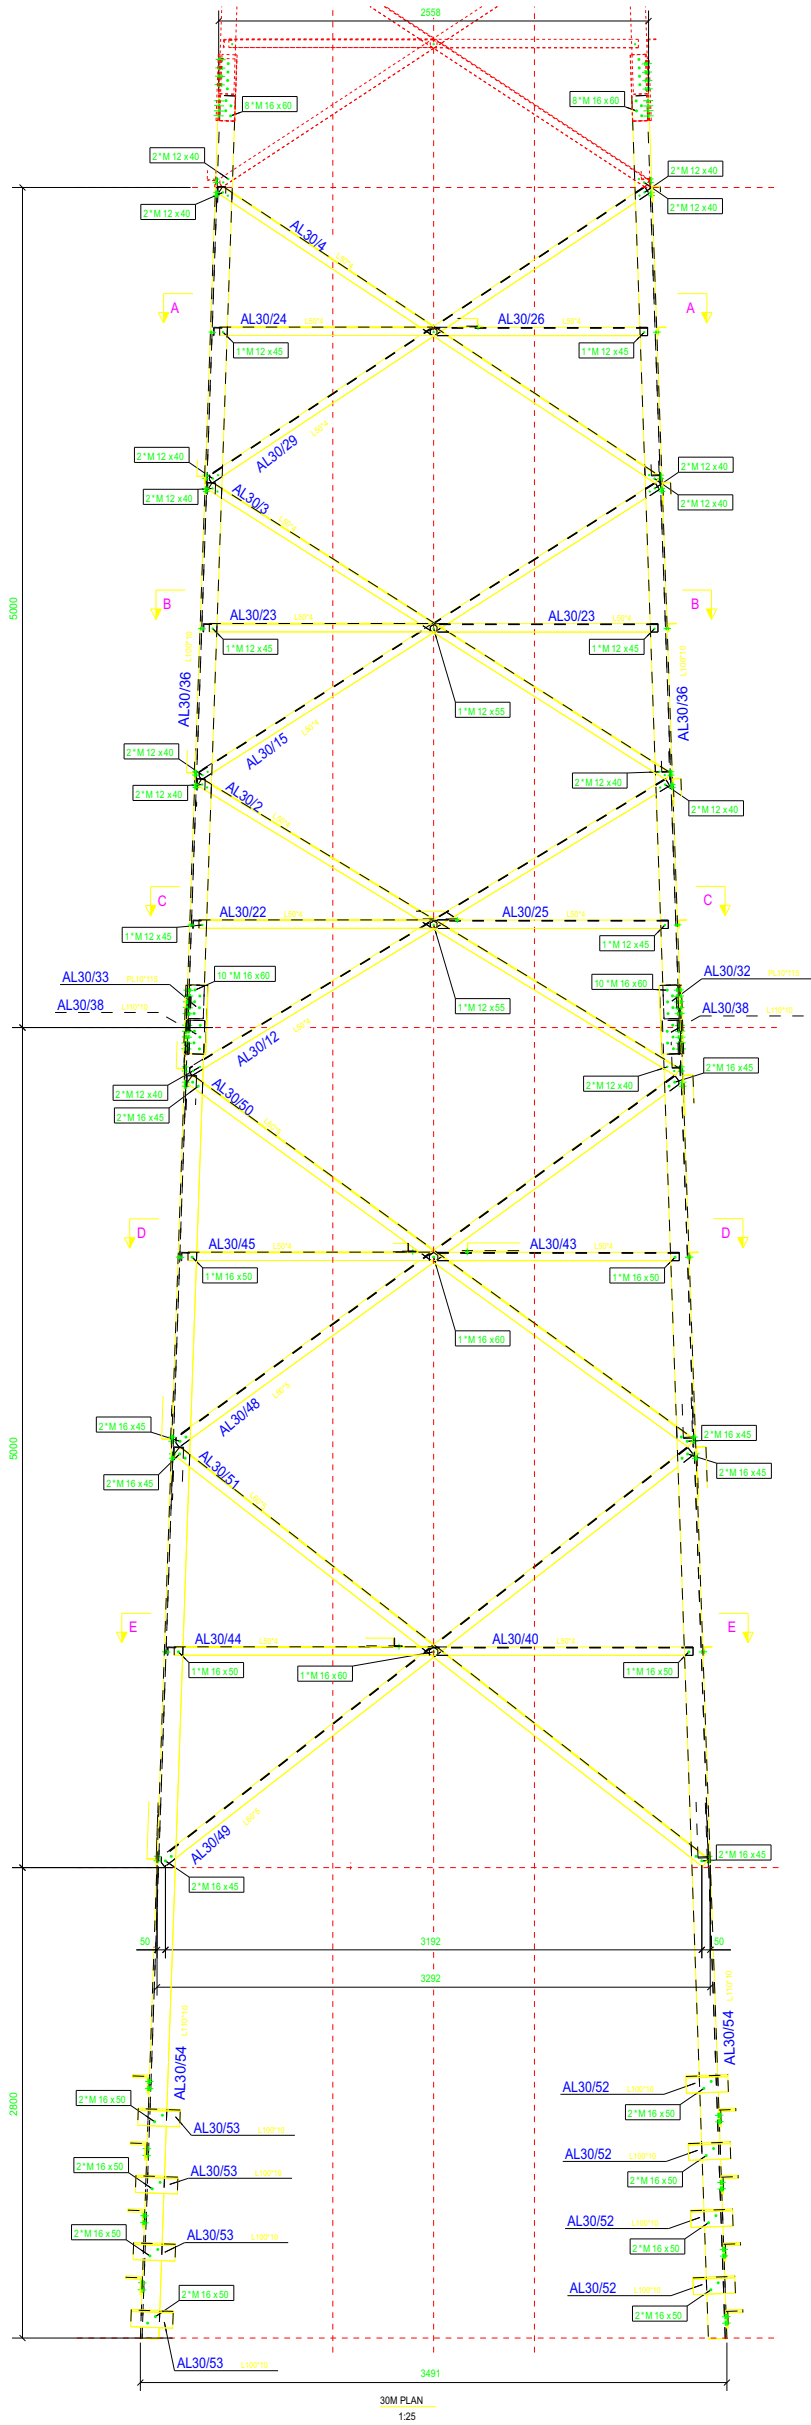

1	0	FOR INFORMATION	09.04.2014
NO	REV	ACIKLAMA	TARİH
TERLEMEZ Machinery			Address: Dağyaka Dist. 2008 St. No: 5 Kazan / Ankara / Turkey
RESİM NO	30M-160-10-003		
YÜKLENİCİ	30M 160-10		
CİZEN	R BAGLAR	TARİH	29.04.2014
YÜKLENİCİ NO	30M 160-10	ÖLÇEK	1:25
DRAWING No	[12]	REVİZYON No.	1

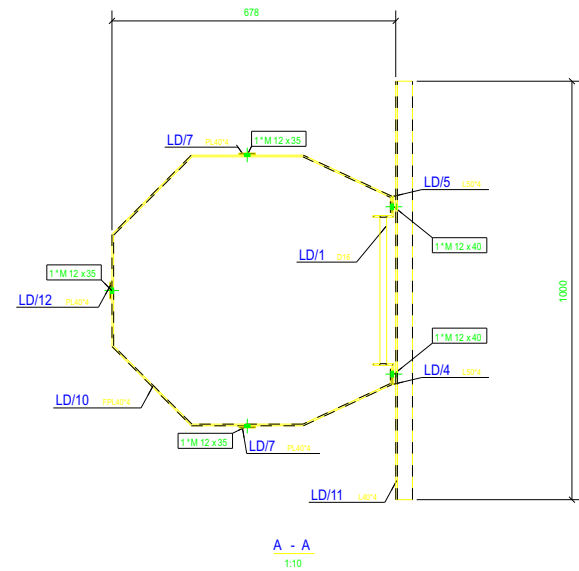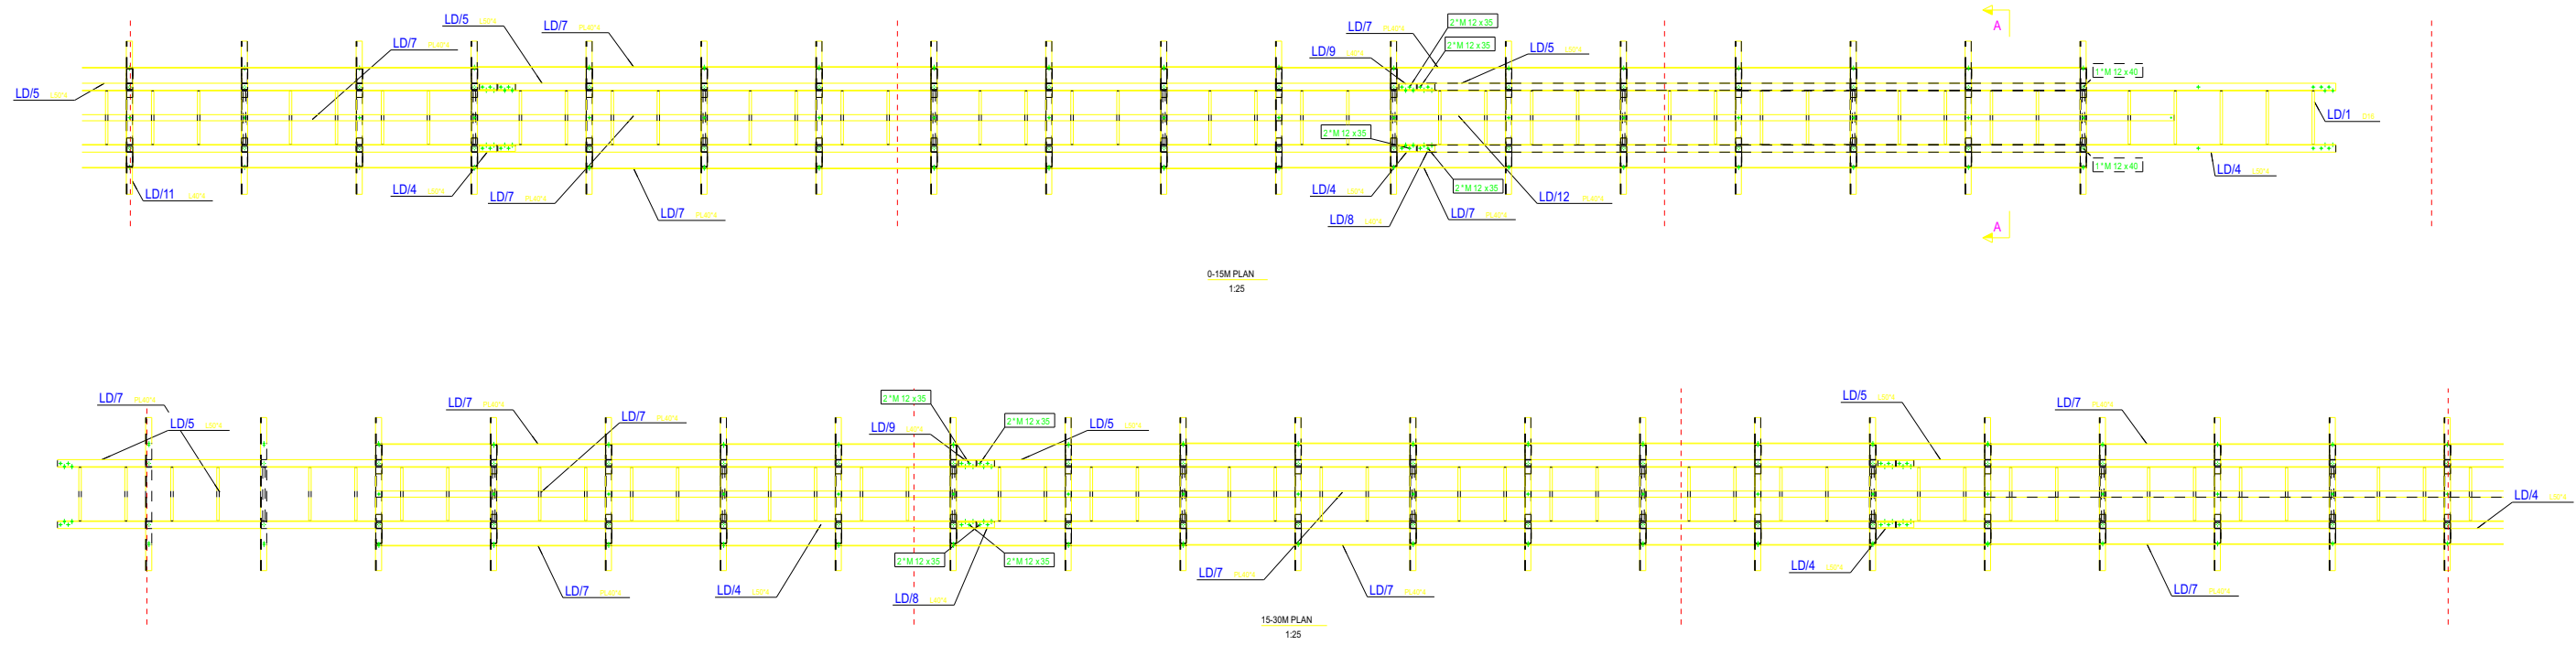

1	0	FOR INFORMATION		09.04.2014
NO	REV	AÇIKLAMA		TARİH
TERLEMEZ Machinery		Address: Dayyaka Dist. 2008 St. No: 5 Kazan / Ankara / Turkey		
RESİM NO	30M-160-10-007			
YÜKLENİCİ	30M 160-10			
ÇİZEN	R BAĞLAR	TARİH	29.04.2014	
YÜKLENİCİ NO	30M 160-10	ÖLÇEK	1:10	1:25
DRAWING No	[8]	REVİZYON No.	1	